



Republika e Kosovës  
Republika Kosova-Republic of Kosova  
Qeveria -Vlada-Government

Ministria e Mjedisit dhe Planifikimit Hapësinor /Ministarstvo Sredine i Prostornog Planiranja/Ministry of Environment and Spatial Planning

AGJENCIA KADASTRALE E KOSOVËS/ KATASTARSKA AGENCIJA KOSOVA/ KOSOVA CADASTRAL AGENCY

Zyra kadastrale komunale / Opštinska katastarska kancelarija: Viti


Nr. i njësisë kadastrale / Br. katastarske jedinice : 02500-0  
178/2026

Zona kadastrale / Katastarska zona: Sllatinë

Numri i lëndës / Broj predmeta: 141/1172-140/26

Lloji i njësisë kadastrale / Vrsta katastarske jedinice : Parcel

Shkalla e zvoglimit / Razmera plana : 1:1250

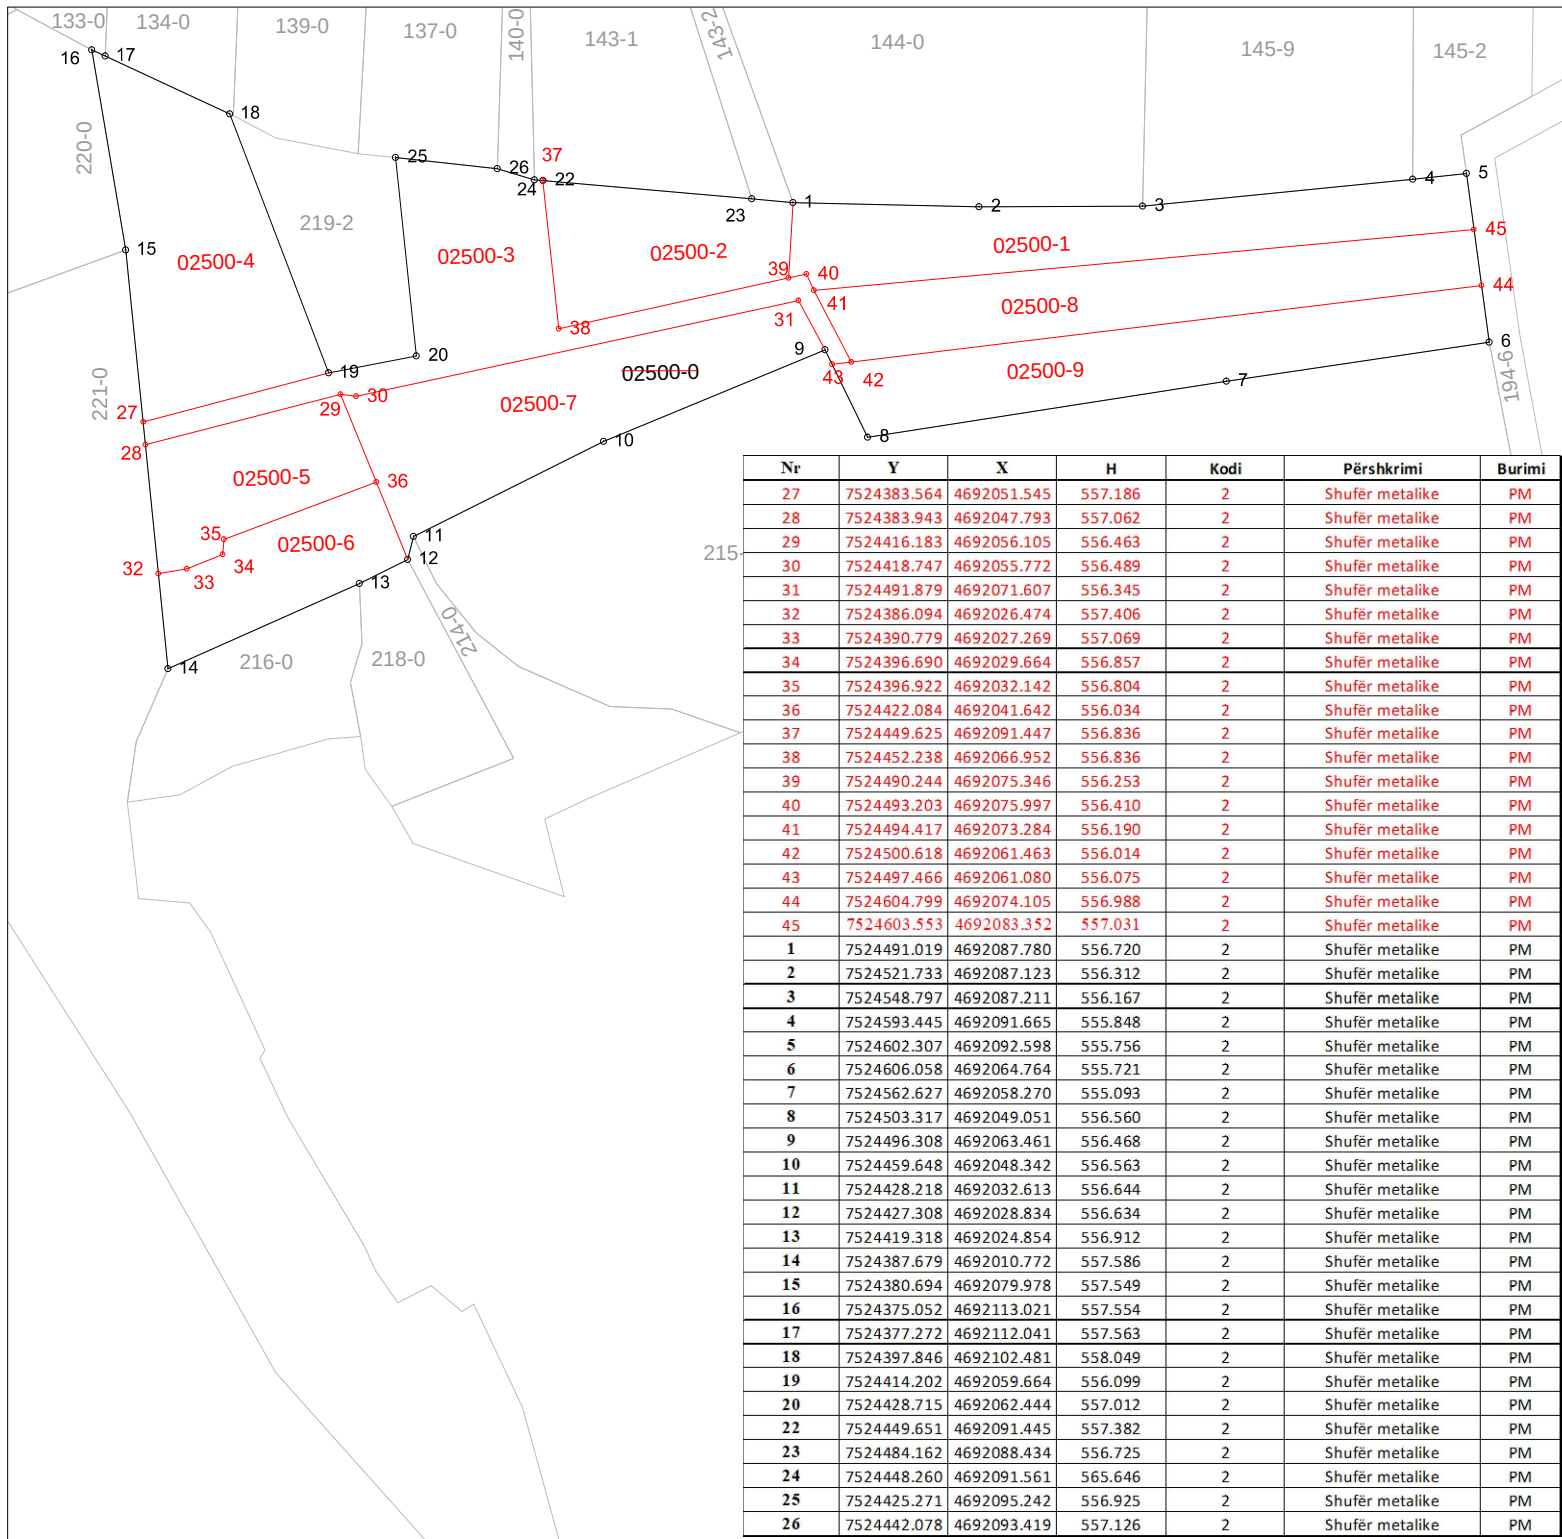

Rilevoi / Snimio: LIRIDON SEJDIU  
(emri dhe mbiemri i gjeodetit/kompanisë/ ime i prezime geodeta/ kompanije)

Aprovoi / Usvojio:  
(emri dhe mbiemri i përsositorit zyrtar/ ime i prezime shërbëtorit lica)

Nr. i licencës / Br. licence: 140

V.V.

Nënshkrimi / Potpis:

Data e rilevimit / Datum snimanja: 09.06.2026

Data e aprovimit / Datum usvajanja: