Republika e Kosovës
Republika Kosova-Republic of Kosova
Qeveria -Vlada-Government
Ministria e Mjedisit dhe Planifikimit Hapësinor /Ministarstvo Sredine i Prostornog Planiranja/Ministry of Environment and Spatial Planning
AGJENCIA KADASTRALE E KOSOVËS/ KATASTARSKA AGECIJA KOSOVA/ KOSOVA CADASTRAL AGENCY

Zyra kadastrale komunale / Opštinska katastarska kancelarija: Viti


Nr. i njësisë kadastrale / Br. katastarske jedinice : 00219-1
00219-3

Zona kadastrale / Katastarska zona: Sllatinë

Numri i lëndës / Broj predmeta: 141/1172-140/26

Lloji i njësisë kadastrale / Vrsta katastarske jedinice : Parcel

Shkalla e zvoglimit / Razmera plana : 1:1250

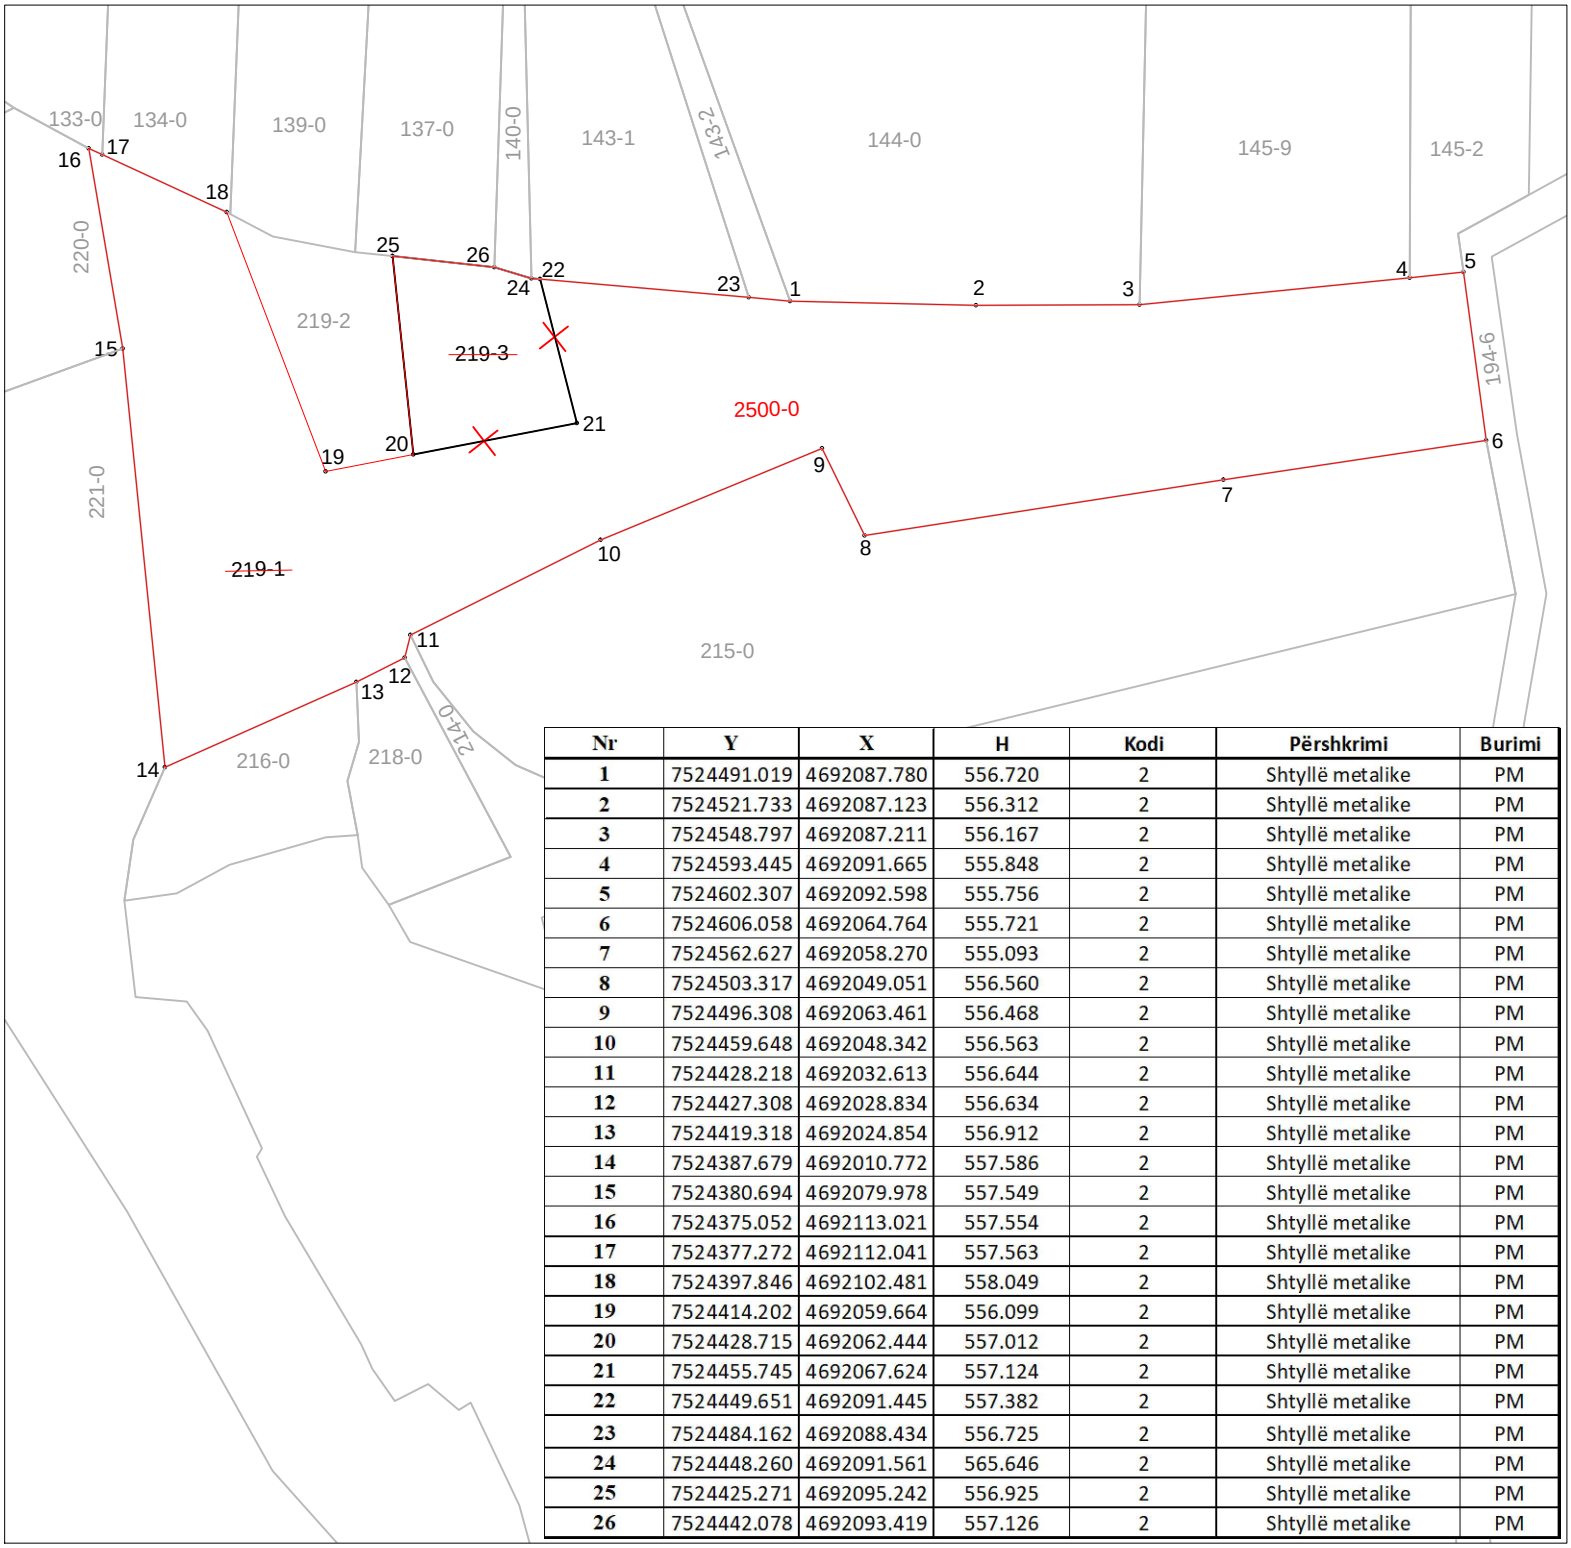

Nr	Y	X	H	Kodi	Përshkrimi	Burimi
1	7524491.019	4692087.780	556.720	2	Shtyllë metalike	PM
2	7524521.733	4692087.123	556.312	2	Shtyllë metalike	PM
3	7524548.797	4692087.211	556.167	2	Shtyllë metalike	PM
4	7524593.445	4692091.665	555.848	2	Shtyllë metalike	PM
5	7524602.307	4692092.598	555.756	2	Shtyllë metalike	PM
6	7524606.058	4692064.764	555.721	2	Shtyllë metalike	PM
7	7524562.627	4692058.270	555.093	2	Shtyllë metalike	PM
8	7524503.317	4692049.051	556.560	2	Shtyllë metalike	PM
9	7524496.308	4692063.461	556.468	2	Shtyllë metalike	PM
10	7524459.648	4692048.342	556.563	2	Shtyllë metalike	PM
11	7524428.218	4692032.613	556.644	2	Shtyllë metalike	PM
12	7524427.308	4692028.834	556.634	2	Shtyllë metalike	PM
13	7524419.318	4692024.854	556.912	2	Shtyllë metalike	PM
14	7524387.679	4692010.772	557.586	2	Shtyllë metalike	PM
15	7524380.694	4692079.978	557.549	2	Shtyllë metalike	PM
16	7524375.052	4692113.021	557.554	2	Shtyllë metalike	PM
17	7524377.272	4692112.041	557.563	2	Shtyllë metalike	PM
18	7524397.846	4692102.481	558.049	2	Shtyllë metalike	PM
19	7524414.202	4692059.664	556.099	2	Shtyllë metalike	PM
20	7524428.715	4692062.444	557.012	2	Shtyllë metalike	PM
21	7524455.745	4692067.624	557.124	2	Shtyllë metalike	PM
22	7524449.651	4692091.445	557.382	2	Shtyllë metalike	PM
23	7524484.162	4692088.434	556.725	2	Shtyllë metalike	PM
24	7524448.260	4692091.561	565.646	2	Shtyllë metalike	PM
25	7524425.271	4692095.242	556.925	2	Shtyllë metalike	PM
26	7524442.078	4692093.419	557.126	2	Shtyllë metalike	PM

Rilevoi / Snimio: LIRIDON SEJDIU
(emri dhe mbiemri i gjeodetit/kompanisë/ ime i prezime geodeta/ kompanije)

Nr. i licencës / Br. licence: 140

Nënshkrimi / Potpis: _____

Data e rilevimit / Datum snimanja: 09.06.2026

V.V.

Aprovoi / Usvojio: _____
(emri dhe mbiemri i përsonit zyrtar/ ime i prezime sluzbenog lica)

Nënshkrimi / Potpis: _____

Data e aprovimit / Datum usvajanja: _____