



Republika e Kosovës
Republika Kosova-Republic of Kosovo
Qeveria - Vlada-Government

Ministria e Mjedisit dhe Planifikimit Hapësinor /Ministarstvo Sredine i Prostornog Planiranja/Ministry of Environment and Spatial Planning
AGJENCIA KADASTRALE E KOSOVËS/ KATASTARSKA AGENCIJA KOSOVA/ KOSOVA CADASTRAL AGENCY

Zyra kadastrale komunale / Opštinska katastarska kancelarija: Viti


Nr. i njësisë kadastrale / Br. katastarske jedinice : 02500-0

Zona kadastrale / Katastarska zona: Sllatinë

Numri i lëndës / Broj predmeta: 141/1172-140/26

Lloji i njësisë kadastrale / Vrsta katastarske jedinice : Parcel

Shkalla e zvoglimit / Razmera plana : 1:1250

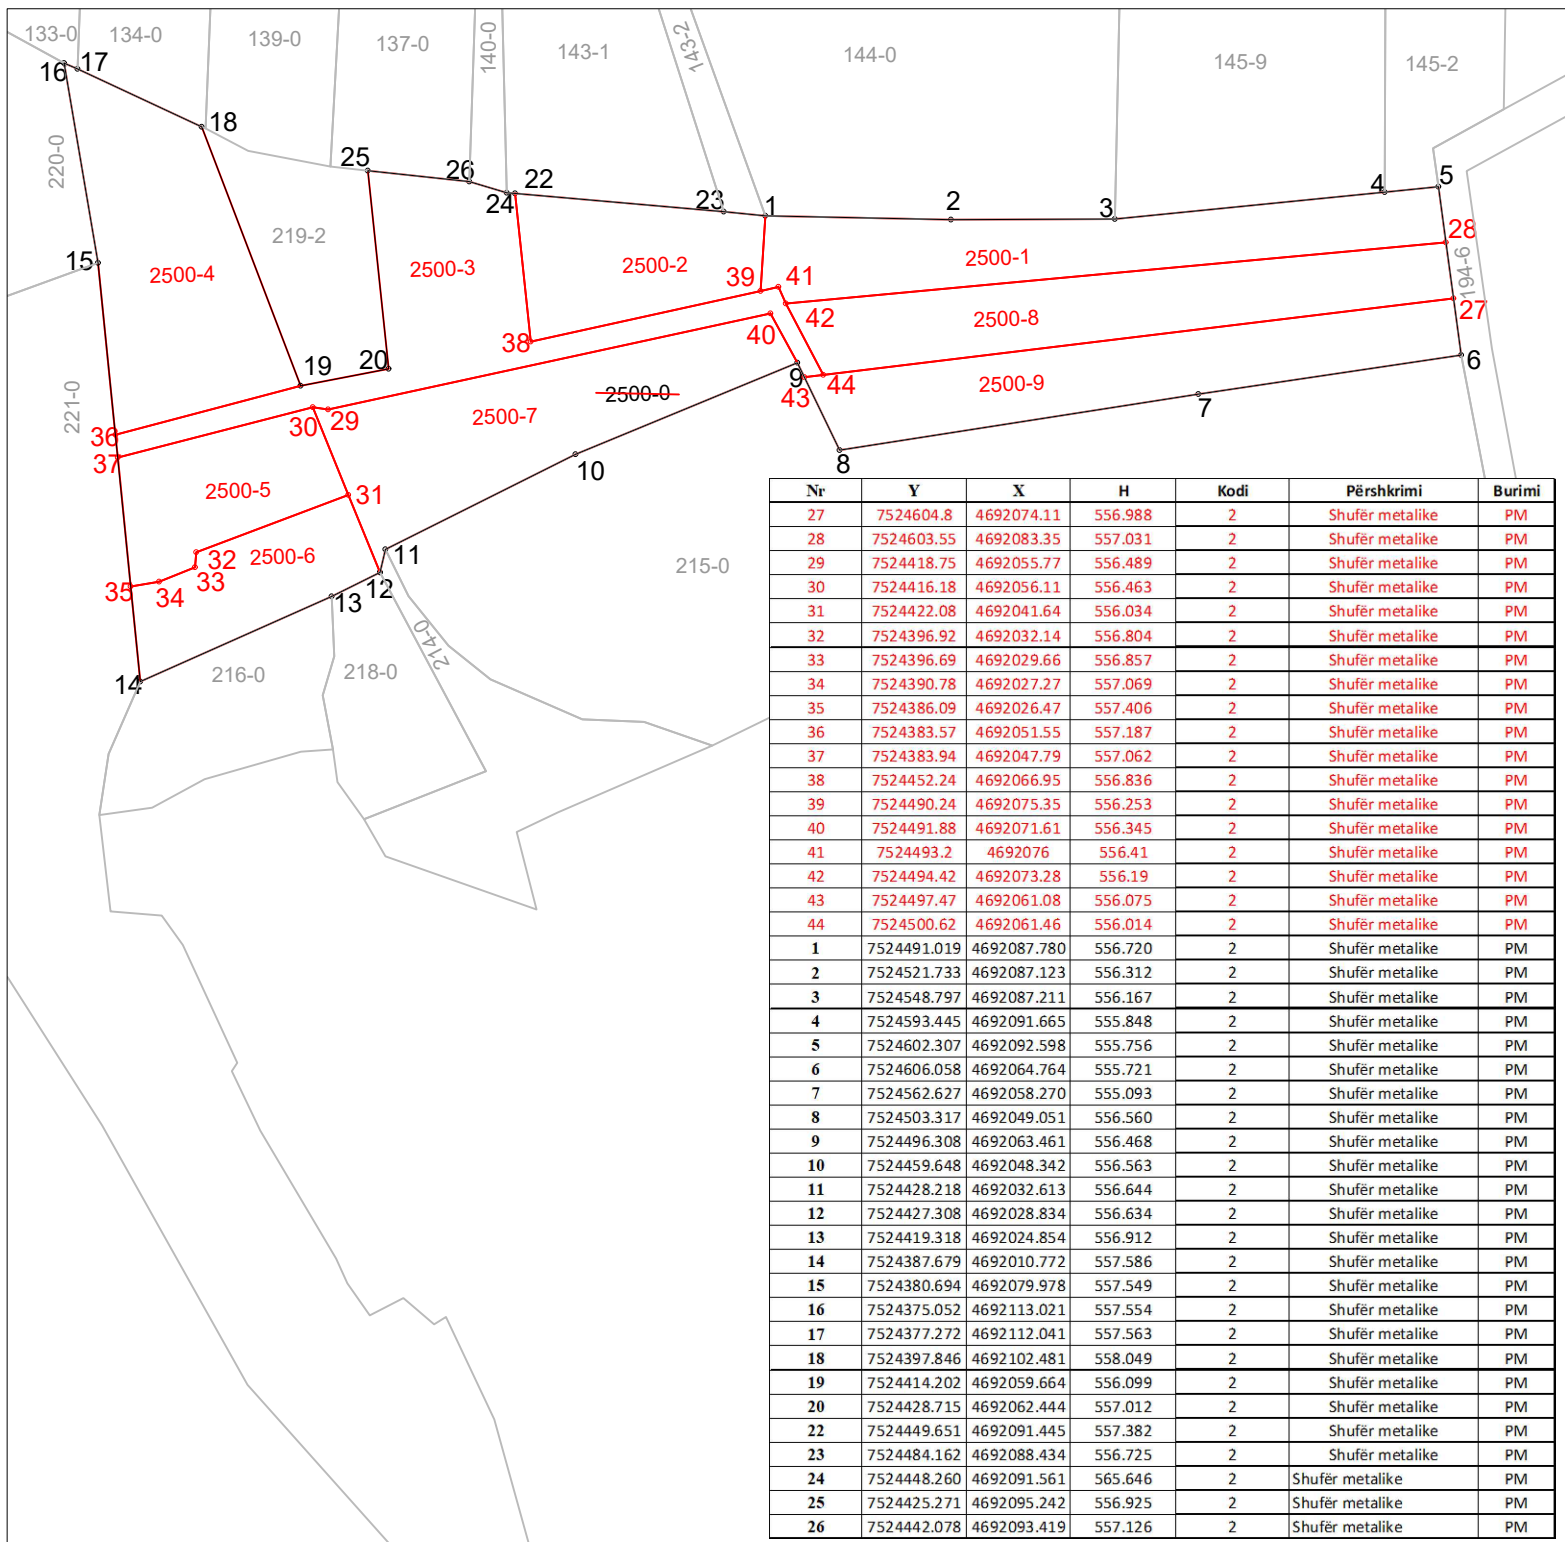

Nr	Y	X	H	Kodi	Përshkrimi	Burimi
27	7524604.8	4692074.11	556.988	2	Shufër metalike	PM
28	7524603.55	4692083.35	557.031	2	Shufër metalike	PM
29	7524418.75	4692055.77	556.489	2	Shufër metalike	PM
30	7524416.18	4692056.11	556.463	2	Shufër metalike	PM
31	7524422.08	4692041.64	556.034	2	Shufër metalike	PM
32	7524396.92	4692032.14	556.804	2	Shufër metalike	PM
33	7524396.69	4692029.66	556.857	2	Shufër metalike	PM
34	7524390.78	4692027.27	557.069	2	Shufër metalike	PM
35	7524386.09	4692026.47	557.406	2	Shufër metalike	PM
36	7524383.57	4692051.55	557.187	2	Shufër metalike	PM
37	7524383.94	4692047.79	557.062	2	Shufër metalike	PM
38	7524452.24	4692066.95	556.836	2	Shufër metalike	PM
39	7524490.24	4692075.35	556.253	2	Shufër metalike	PM
40	7524491.88	4692071.61	556.345	2	Shufër metalike	PM
41	7524493.2	4692076	556.41	2	Shufër metalike	PM
42	7524494.42	4692073.28	556.19	2	Shufër metalike	PM
43	7524497.47	4692061.08	556.075	2	Shufër metalike	PM
44	7524500.62	4692061.46	556.014	2	Shufër metalike	PM
1	7524491.019	4692087.780	556.720	2	Shufër metalike	PM
2	7524521.733	4692087.123	556.312	2	Shufër metalike	PM
3	7524548.797	4692087.211	556.167	2	Shufër metalike	PM
4	7524593.445	4692091.665	555.848	2	Shufër metalike	PM
5	7524602.307	4692092.598	555.756	2	Shufër metalike	PM
6	7524606.058	4692064.764	555.721	2	Shufër metalike	PM
7	7524562.627	4692058.270	555.093	2	Shufër metalike	PM
8	7524503.317	4692049.051	556.560	2	Shufër metalike	PM
9	7524496.308	4692063.461	556.468	2	Shufër metalike	PM
10	7524459.648	4692048.342	556.563	2	Shufër metalike	PM
11	7524428.218	4692032.613	556.644	2	Shufër metalike	PM
12	7524427.308	4692028.834	556.634	2	Shufër metalike	PM
13	7524419.318	4692024.854	556.912	2	Shufër metalike	PM
14	7524387.679	4692010.772	557.586	2	Shufër metalike	PM
15	7524380.694	4692079.978	557.549	2	Shufër metalike	PM
16	7524375.052	4692113.021	557.554	2	Shufër metalike	PM
17	7524377.272	4692112.041	557.563	2	Shufër metalike	PM
18	7524397.846	4692102.481	558.049	2	Shufër metalike	PM
19	7524414.202	4692059.664	556.099	2	Shufër metalike	PM
20	7524428.715	4692062.444	557.012	2	Shufër metalike	PM
22	7524449.651	4692091.445	557.382	2	Shufër metalike	PM
23	7524484.162	4692088.434	556.725	2	Shufër metalike	PM
24	7524448.260	4692091.561	565.646	2	Shufër metalike	PM
25	7524425.271	4692095.242	556.925	2	Shufër metalike	PM
26	7524442.078	4692093.419	557.126	2	Shufër metalike	PM

Rilevoi / Snimio: LIRIDON SEJDIU
(emri dhe mbiemri i gjeodetit/kompanisë/ ime i prezime gjeodeta/ kompanije)

Aprovoi / Usvojio:
(emri dhe mbiemri i përsorit zyrtar/ ime i prezime shërbëuesit)

Nr. i licencës / Br. licence: 140

V.V.

Nënshkrimi / Potpis:

Nënshkrimi / Potpis:

Data e rievimit / Datum snimanja: 23.03.2026

Data e aprovimit / Datum usvajanja: